


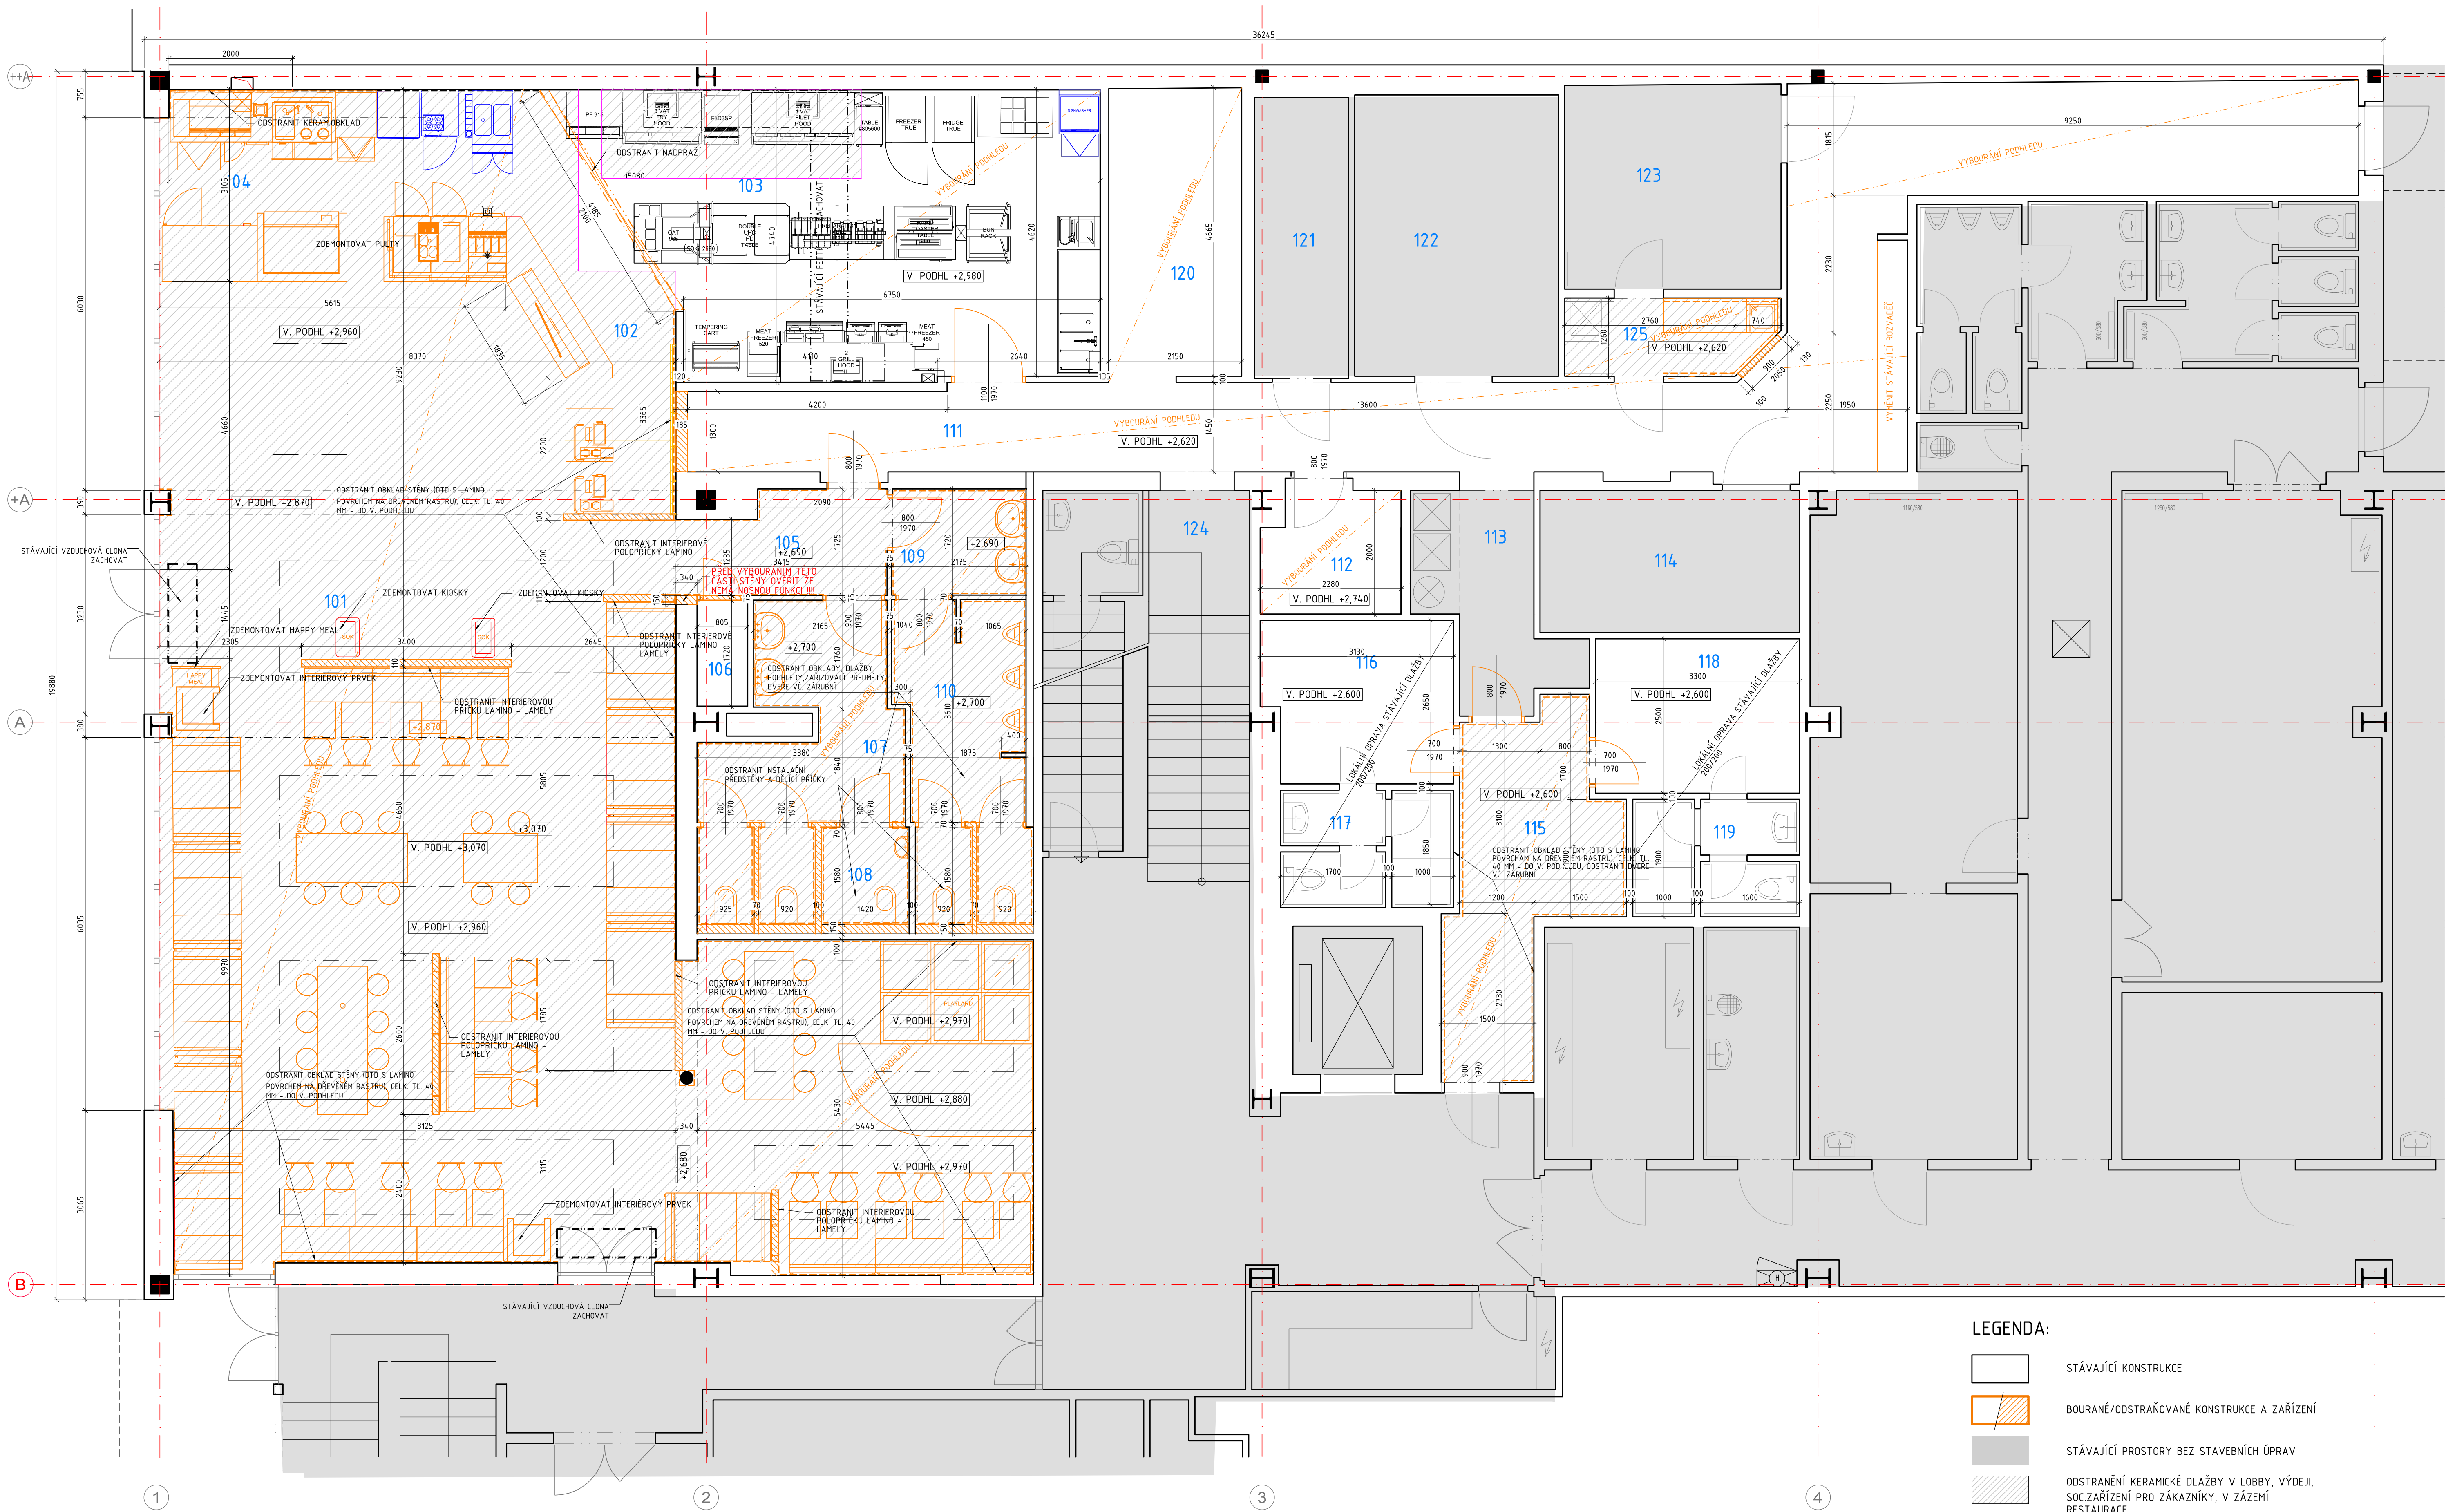

LEGENDA OBJEKTU McD					
číslo míst.	účel místnosti	m2	podlahy	stěny	stropy
101	RESTAURACE/LOBBY	154,85	velkoformátová dlažba	omítka, interiérový obklad	keramit. kazet. podhled
102	VÝDEJ	18,25	velkoformátová dlažba	omítka, interiérový obklad	SDK podhled
103	PŘÍPRAVNA JIDEL	35,50	keramická dlažba protiškluzová	ker. obklad 150/200 bílý dle standardu McDonald's	SDK podhled
104	MCCAFÉ	10,90	velkoformátová dlažba	omítka, interiérový obklad	SDK podhled
105	CHODBA	5,25	velkoformátová dlažba	omítka, interiérový obklad	keramit. kazet. podhled
106	ÚKLID	1,35	—	—	—
107	WC ŽENY	12,00	velkoformátová dlažba	keram.obklad do v.podh.	SDK podhled
108	WC INVALIDŮ	2,25	velkoformátová dlažba	keram.obklad do v.podh.	SDK podhled
109	WC - PŘEDSÍŇKA MUŽI	3,70	velkoformátová dlažba	keram.obklad do v.podh.	SDK podhled
110	WC MUŽI	10,40	velkoformátová dlažba	keram.obklad do v.podh.	SDK podhled
111	CHODBA	48,80	keramická dlažba	malba, obklad, al-plech	kazetový podhled
112	MÍSTNOST MANAGERA	4,50	keramická dlažba	malba	kazetový podhled
113	TECHNICKÁ MÍSTNOST	6,65	—	—	—
114	LISOVNA, SKLAD ODPADU	9,65	—	—	—
115	DENNÍ MÍSTNOST	12,15	velkoformátová dlažba	interiérové obklady	SDK podhled
116	ŠATNA MUŽI	7,85	keramická dlažba	—	—
117	ZAHĚS. UMÝVÁRNA,WC MUŽI	5,00	keramická dlažba	—	—
118	ŠATNA ŽENY	8,25	keramická dlažba	—	—
119	ZAHĚS. UMÝVÁRNA,WC ŽENY	4,90	keramická dlažba	—	—
120	MULTIPLEX	10,20	—	—	kazetový podhled
121	CHLADÍRNA	6,90	—	—	—
122	HRAZÍRNA	15,00	—	—	—
123	SUCHÝ SKLAD	11,50	—	—	—
124	SKLAD	6,00	—	—	—
125	SEPARACE, ÚKLID	4,10	keramická dlažba	keram.obklad do v.podh.	SDK podhled

- POPIS:**
- PŘI BOURACÍCH PRÁČÍCH NUTNO POSTUPOVAT TAK, ABY NEBYLA NARUŠENA ČI POŠKOZENA NOSNÁ KONSTRUKCE OBJEKTU
 - VEŠKERÉ KONSTRUKCE, KTERÉ ZŮSTÁVAJÍ V RÁMCI REKONSTRUKCE ZACHOVÁNY (DVEŘE, OKNA, ZAŘÍZENÍ, KTERÉ ZŮSTÁVÁ APOD.) MUSÍ BÝT PŘED ZAHÁJENÍM REKONSTRUKCE ZABEZPEČENY A OCHRÁNĚNY TAK, ABY NEDOŠLO K JEJICH POŠKOZENÍ A ZNEČIŠTĚNÍ BĚHEM STAVBY
 - PRVKY NEBO TECHNOLOGICKÉ VYBAVENÍ, KTERÉ JSOU DEMONTOVATELNÉ A BUDOU ZNOVU POUŽITY A U KTERÝCH HROZÍ POŠKOZENÍ BĚHEM REKONSTRUKCE, BUDOU PŘED ZAHÁJENÍM REKONSTRUKCE DEMONTOVÁNY A USKLADNĚNY TAK, ABY JE BYLO MOŽNÉ ZNOVU POUŽÍT
 - V PŘÍPADĚ, ŽE PŘI BOURACÍCH PRÁČÍCH BUDOU ZJIŠTĚNY SKUTEČNOSTI ROZDÍLNÉ OPROTÍ PD A SKUTEČNOSTI, SE KTERÝMI PROJEKT NEPOČÍTÁ, BUDOU NEPRODLENĚ OZNÁMENY ŘEŠITELI PD
 - V RÁMCI BOURACÍCH PRÁČÍ JE NUTNO ODSTRANIT VEŠKERÉ VYBAVENÍ V RÁMCI LOBBY (NÁBYTEK, OBJEDNÁVKOVÉ PANELE, PANEL HAPPY MEAL, SVĚTELNÉ REKLAMY V OKNECH A STÍNÍCÍ ŽALUZIE), V RÁMCI KUCHYNĚ PAK KONKRÉTNÍ TECHNOLOGICKÉ ZAŘÍZENÍ DLE PROJEKTU TECHNOLOGIE KUCHYNĚ
 - NA SOCIÁLNÍM ZAŘÍZENÍ PRO ZÁKAZNÍKY BUDOU ODSTRANĚNY VEŠKERÉ ZAŘÍZOVACÍ PŘEDMĚTY VČ.BATERIÍ A SANITÁRNÍ VYBAVENÍ (ZÁSOBNÍKY, KOŠE APOD.)
 - ROZSAH ODSTRANĚNÍ STÁVAJÍCÍ DLAŽBY JE PATRNÝ Z " VÝKRESU DLAŽBY - STÁVAJÍCÍ STAV A BOURÁNÍ"
 - ROZSAH ODSTRANĚNÍ STÁVAJÍCÍCH PODHLADŮ JE PATRNÝ Z " KLADĚČSKÉHO VÝKRESU PODHLADŮ - STÁVAJÍCÍ STAV A DEMONTÁŽE"

LEGENDA:

STÁVAJÍCÍ KONSTRUKCE

BOURANÉ/ODSTRANĚNÉ KONSTRUKCE A ZAŘÍZENÍ

STÁVAJÍCÍ PROSTORY BEZ STAVEBNÍCH ÚPRAV

ODSTRANĚNÍ KERAMICKÉ DLAŽBY V LOBBY, VÝDEJI, SOC ZAŘÍZENÍ PRO ZÁKAZNÍKY, V ZÁZEMÍ RESTAURACE

Číslo revize/datum		Výpracoval		Proje	
—		—		—	
—		—		—	
—		—		—	
—		—		—	
± 0,000 = stávající m.n.m. Bp					
Investor					
McDonald's ČR spol. s r.o., IČ: 161 91 129 Radlická 740/113c, 158 00 Praha 5			Generální projektant		
			Zodpovědný projektant		
			HIP		
			Ing. arch. P. Lupač, Ph.D. Ing. Daniela Maxová		
Akce					
MODERNIZACE INTERIÉRU PROVOZOVNĚ RESTAURACE MCDONALD'S, ČESKÉ BUDĚJOVICE II LANNOVA TR. 1461/22, 370 01 ČESKÉ BUDĚJOVICE			Zpracovatel části		
			Stoh Consulting, s.r.o.		
			Ing. arch. P. Lupač, Ph.D. Ing. Daniela Maxová		
			Výpracoval		
			Kontakt		
			Číslo paré		
Číslo dokumentace			Číslo zakázky		
D.1.1 ARCHITEKTONICKO STAVEBNÍ ŘEŠENÍ			2510_03		
			Datum		
			02/2026		
			Stupeň		
			DPS		
			Číslo části		
			D.1.1.2		
Obsah					
Měřítko			Formát		
1 : 50			10 x A4		
Revize/Datum			Číslo výkresu		
00/-			01		
PŮDORYS 1. NP – BOURANÉ KONSTRUKCE					