
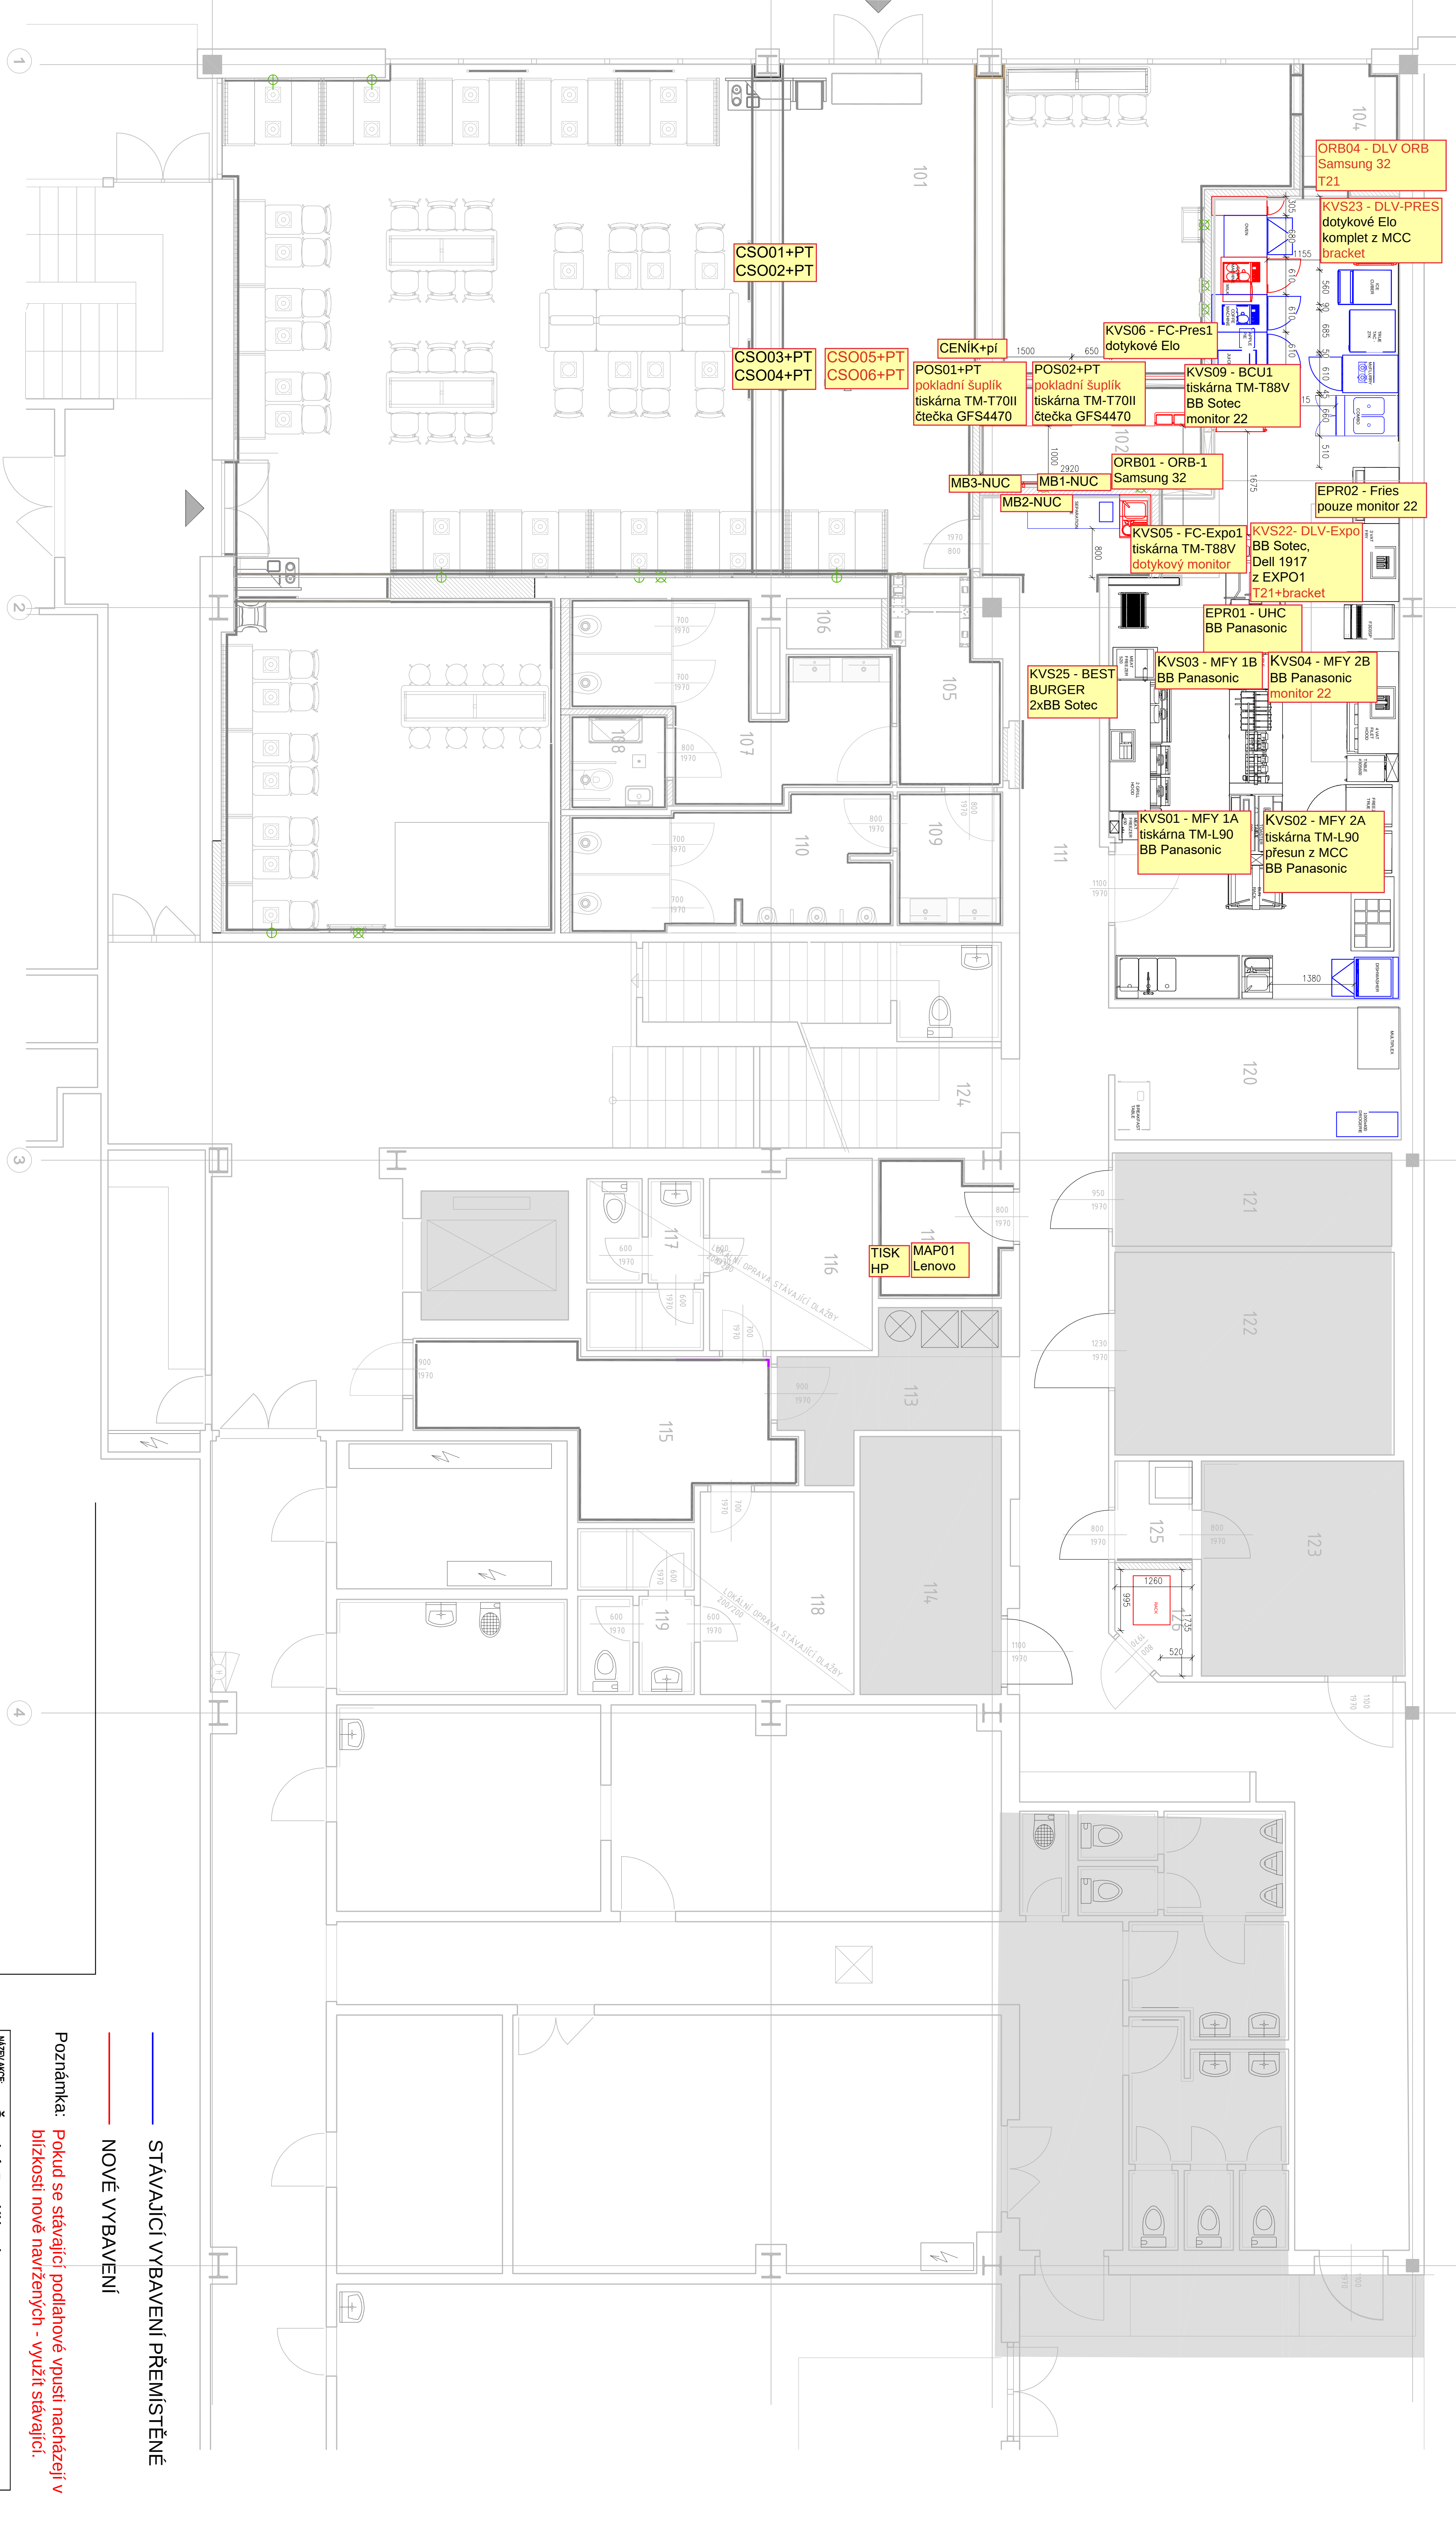


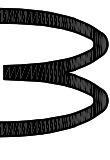

STÁVAJÍCÍ VYBAVENÍ PŘEMÍSTĚNÉ

NOVÉ VYBAVENÍ

Poznámka: Pokud se stávající podlahové vpusti nacházejí v blízkosti nové navýšených - využít stávající.

NÁZEV AKCE:		České Budějovice II	
		RESTAURACE McDonald's	
		Lamnova tř. 1461/22, 37001 České Budějovice	
GENERÁLNÍ PROJEKTANT:	INVESTOR:	PŘÍJÍM:	
stoh consulting	 McDonald's ČR spol. s r.o. Rudská 1461/12c, 158 00, Praha 5 IČO:31802239	14.04.2026	
STUPEŇ DOKUMENTACE:			
Dokumentace pro povolení stavby			
ČÁST DOKUMENTACE:		PRŮJEMNÁ PROJEKT s.r.o. Průmyslová 272/96 IČO:24715671	
VYPRACOVAL:	PODPIS:	1:50	
Kateřina Dyrnová			
KONTROLOVAL:	PODPIS:		
Nikola Masopustová		K1	
VÝKRES:			
VÝKRES ZAŘÍZENÍ KUCHYNĚ			
AI			
POZNÁMKA:	MĚŘITKO:	Č. VÝKRESU	
	1:50		